


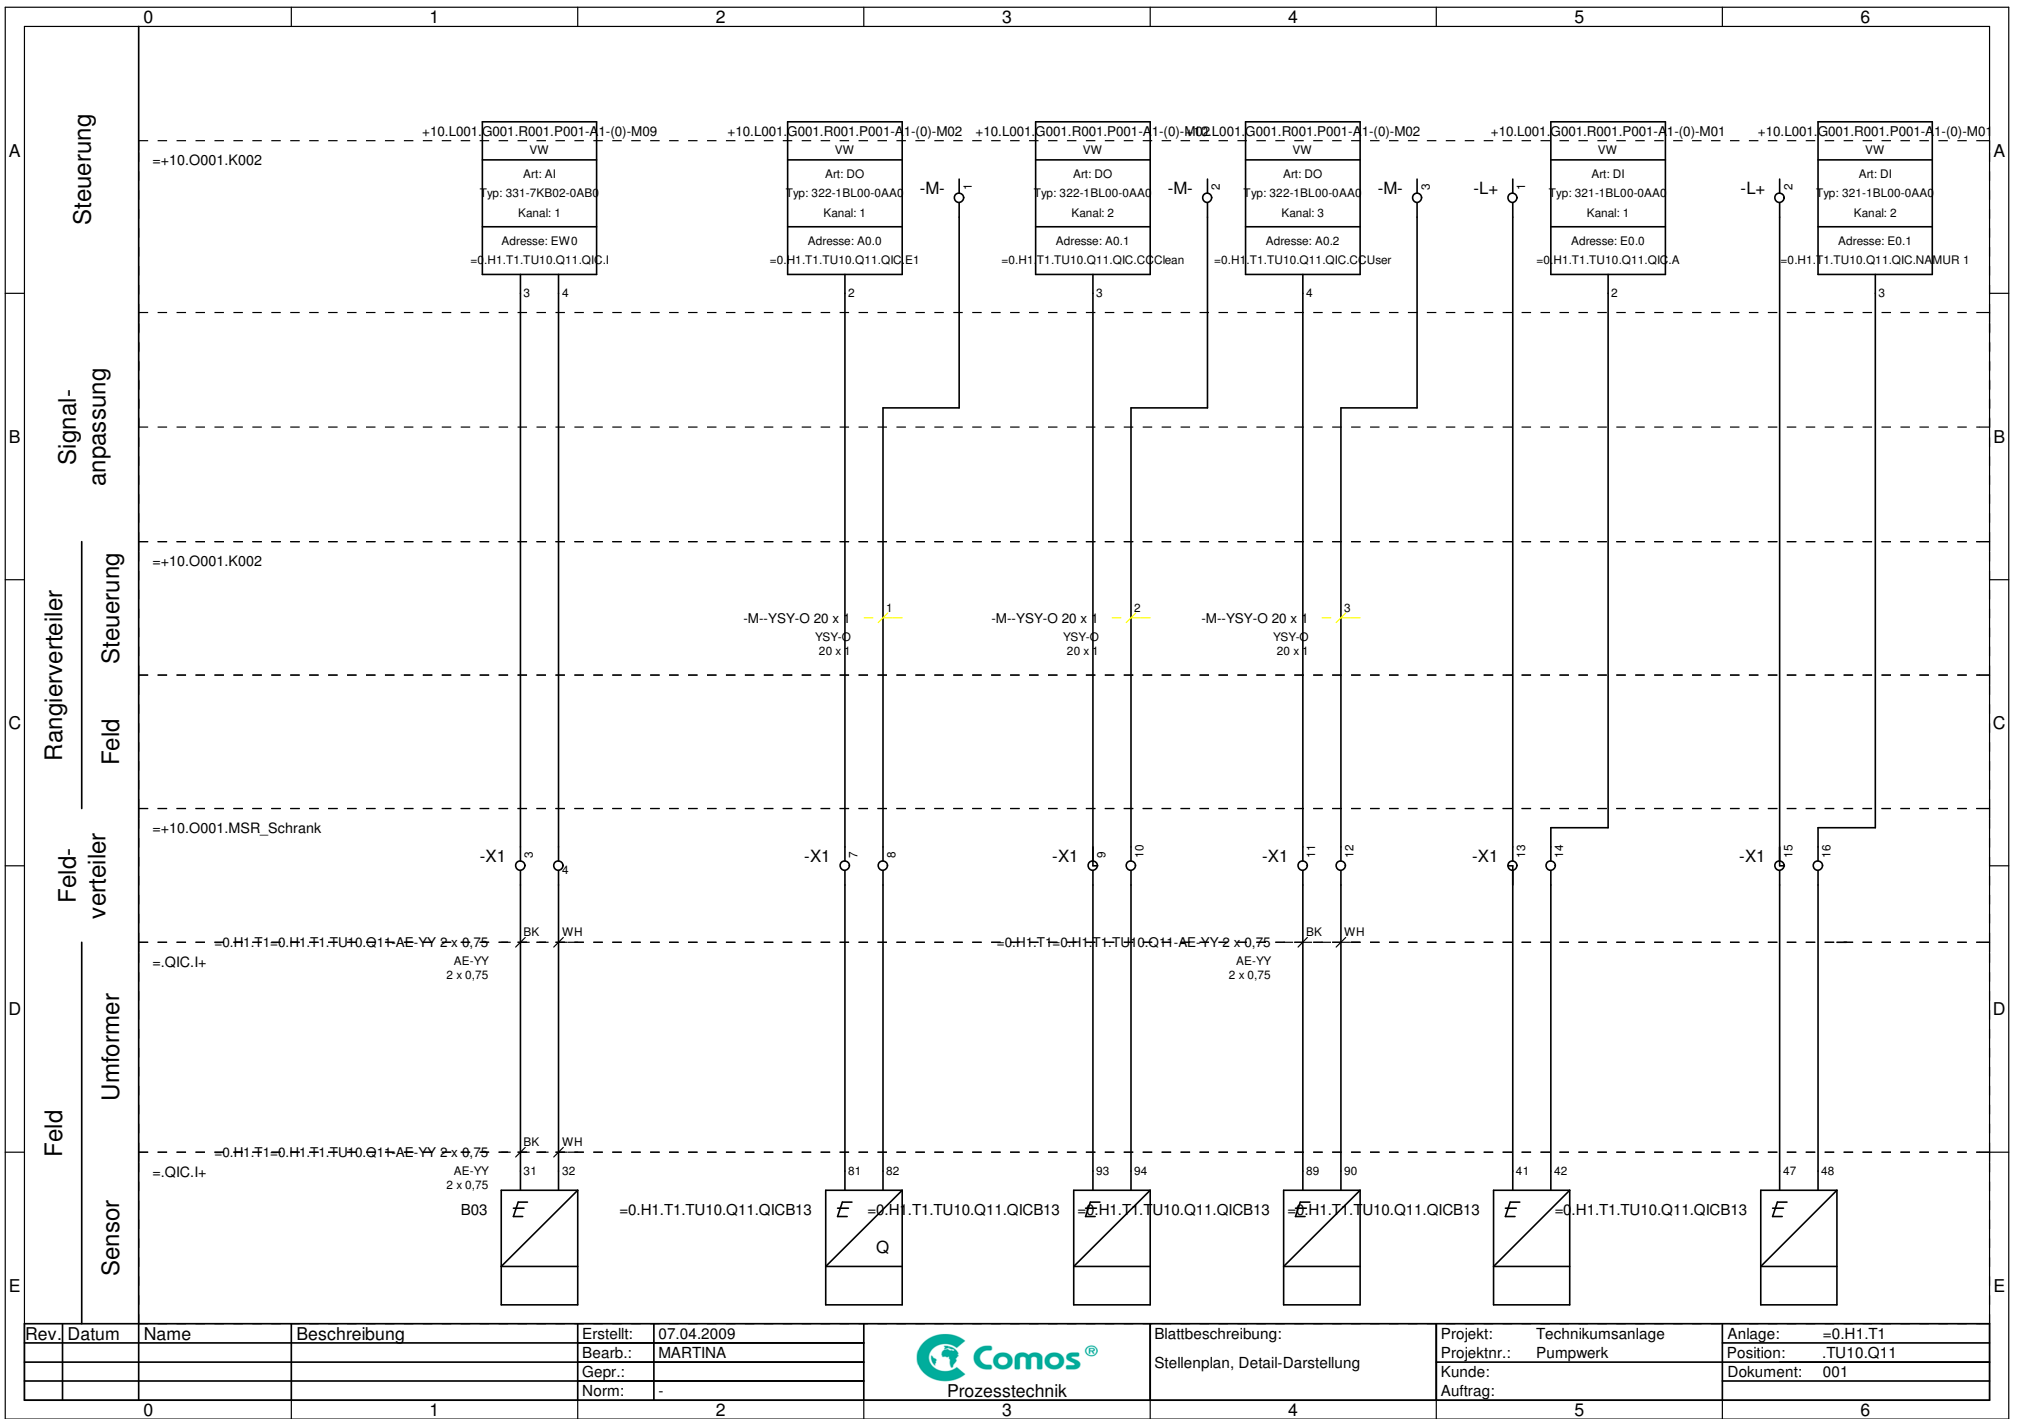

| Rev. | Datum | Name | Beschreibung | Erstellt: | 07.04.2009 |
|------|-------|------|--------------|-----------|------------|
|      |       |      |              | Bearb.:   | MARTINA    |
|      |       |      |              | Gepr.:    |            |
|      |       |      |              | Norm:     | -          |



|                                 |             |                  |           |           |
|---------------------------------|-------------|------------------|-----------|-----------|
| Blattbeschreibung:              | Projekt:    | Technikumsanlage | Anlage:   | =0.H1.T1  |
| Stellenplan, Detail-Darstellung | Projektnr.: | Pumpwerk         | Position: | .TU10.Q11 |
|                                 | Kunde:      |                  | Dokument: | 001       |
|                                 | Auftrag:    |                  |           |           |

