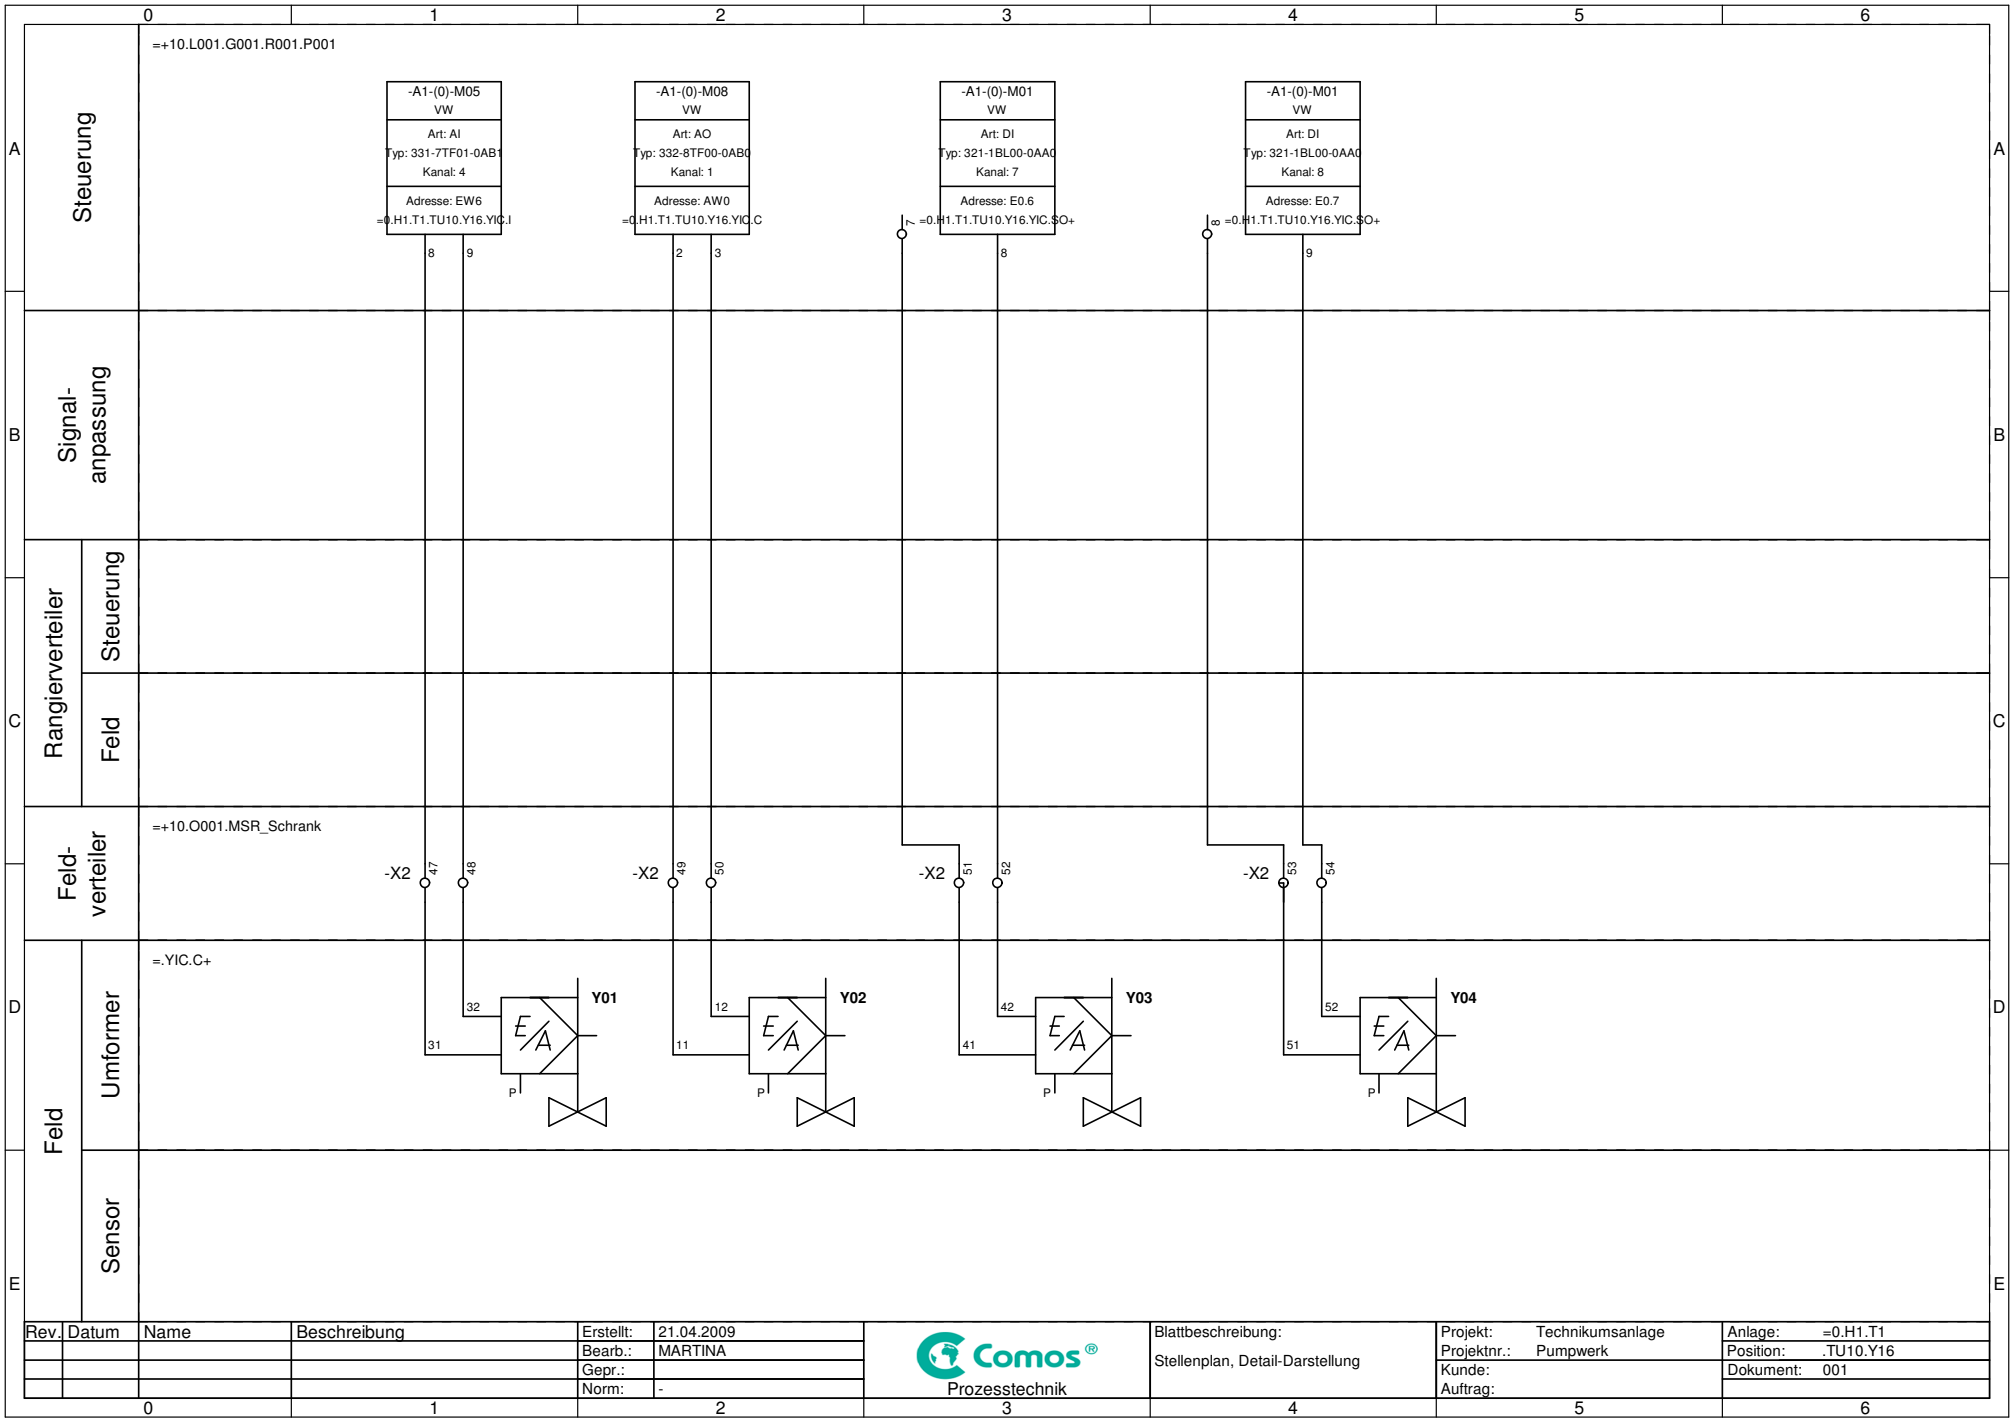

Rev.	Datum	Name	Beschreibung						
				Erstellt:	21.04.2009	Comos® Prozesstechnik	Blattbeschreibung: Stellenplan, Detail-Darstellung	Projekt: Technikumsanlage	Anlage: =0.H1.T1
				Bearb.:	MARTINA			Projektnr.: Pumpwerk	Position: .TU10.Y16
				Gepr.:				Kunde:	Dokument: 001
				Norm:	-			Auftrag:	