


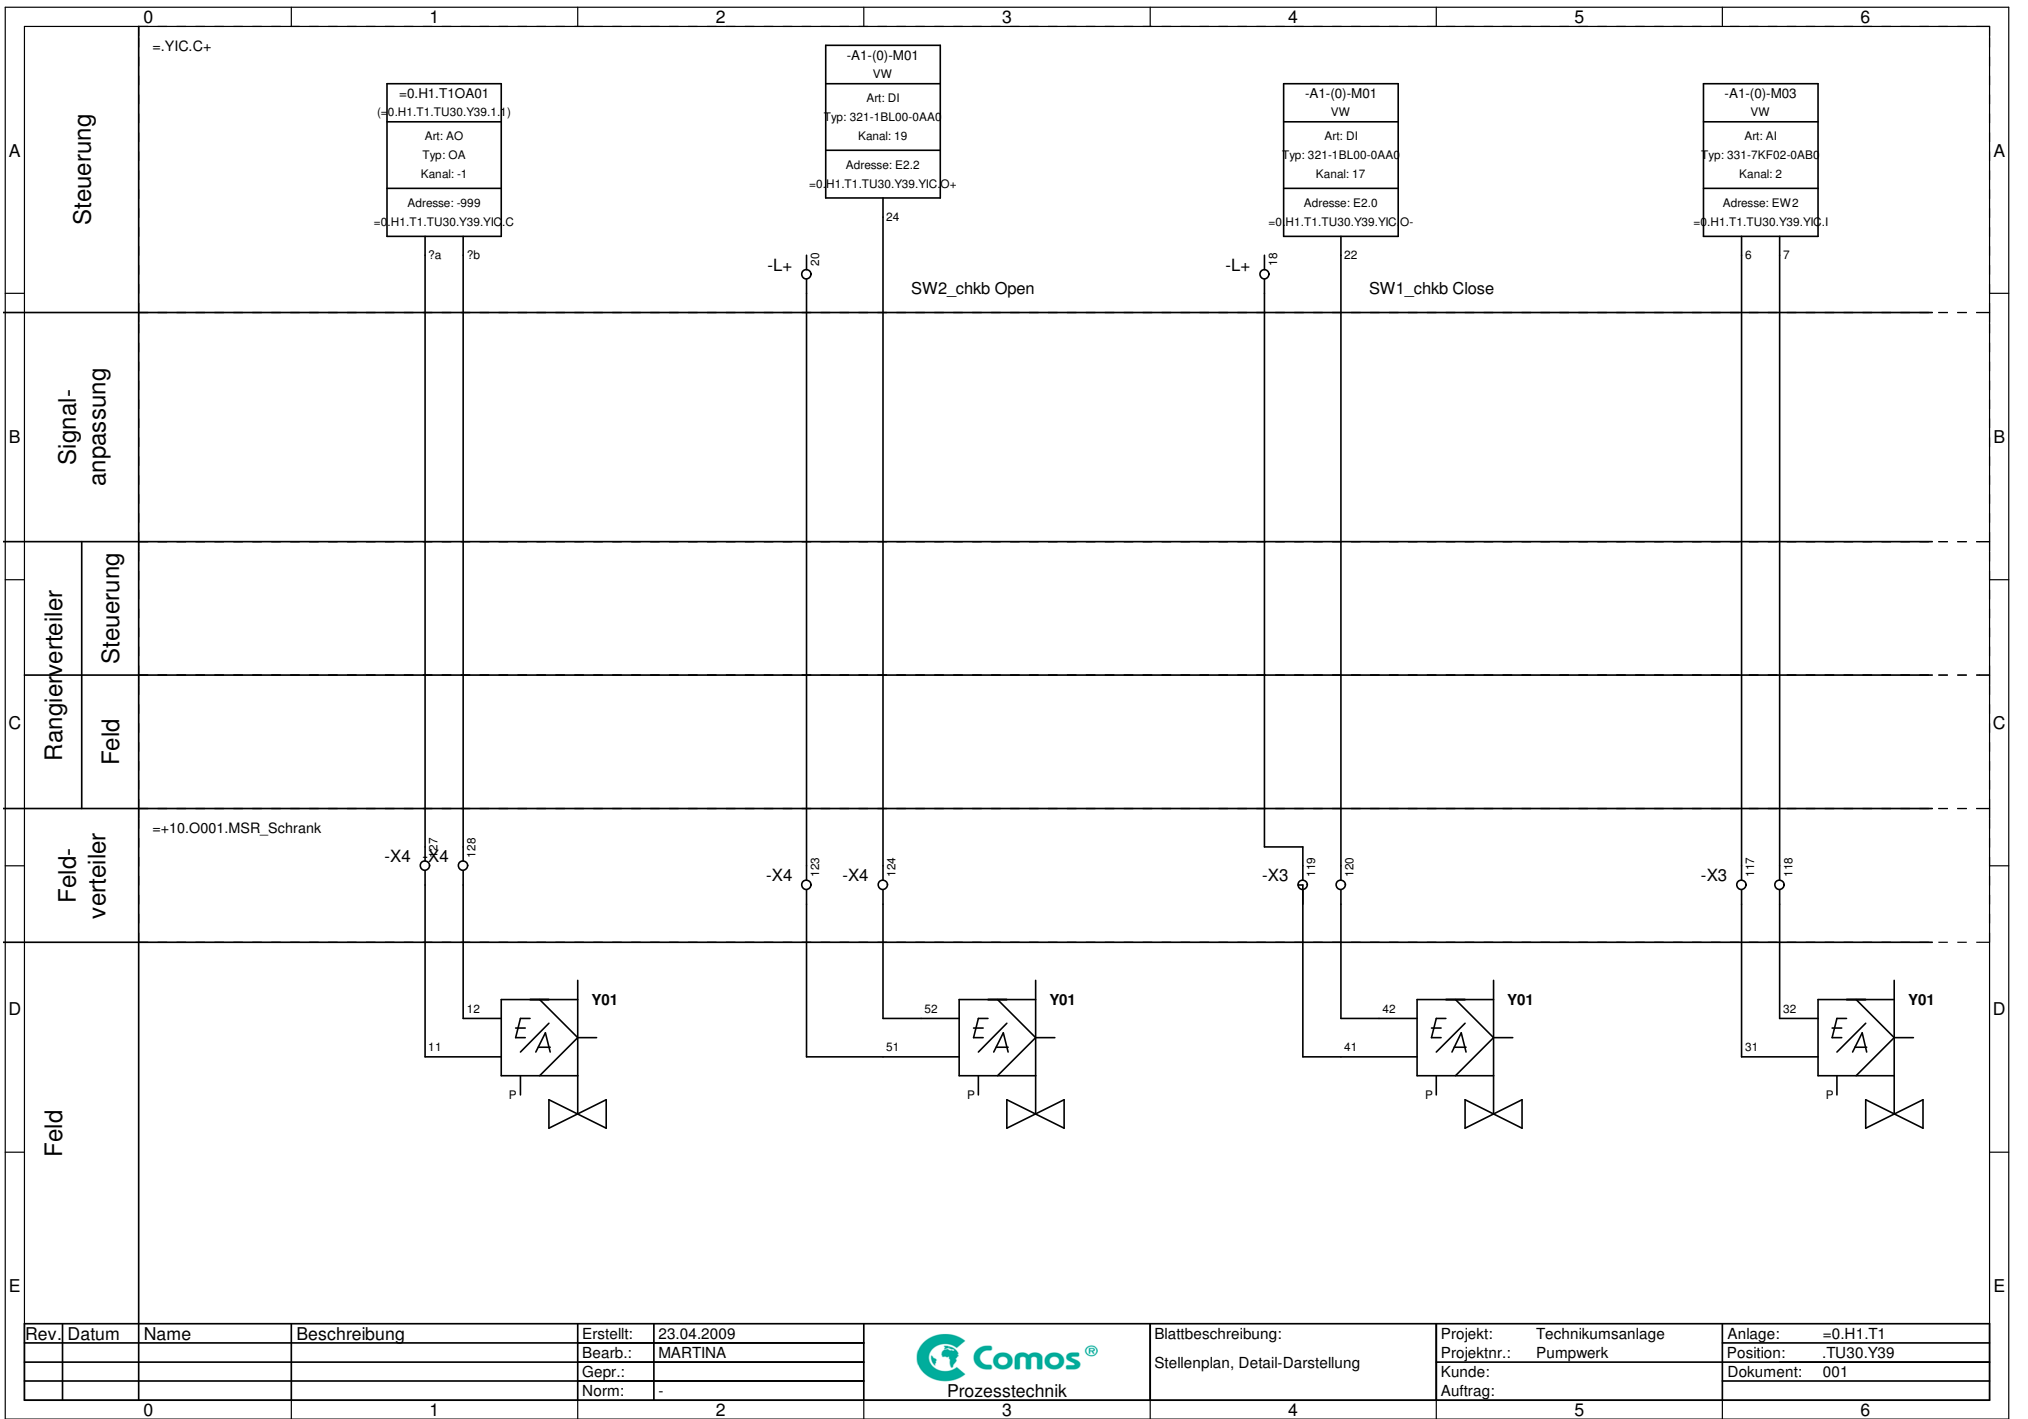

Rev.	Datum	Name	Beschreibung	Erstellt:	23.04.2009
				Bearb.:	MARTINA
				Gepr.:	
				Norm:	-



Blattbeschreibung:
Stellenplan, Detail-Darstellung

Projekt: Technikumsanlage
Projektnr.: Pumpwerk
Kunde:
Auftrag:

Anlage: =0.H1.T1
Position: .TU30.Y39
Dokument: 001

