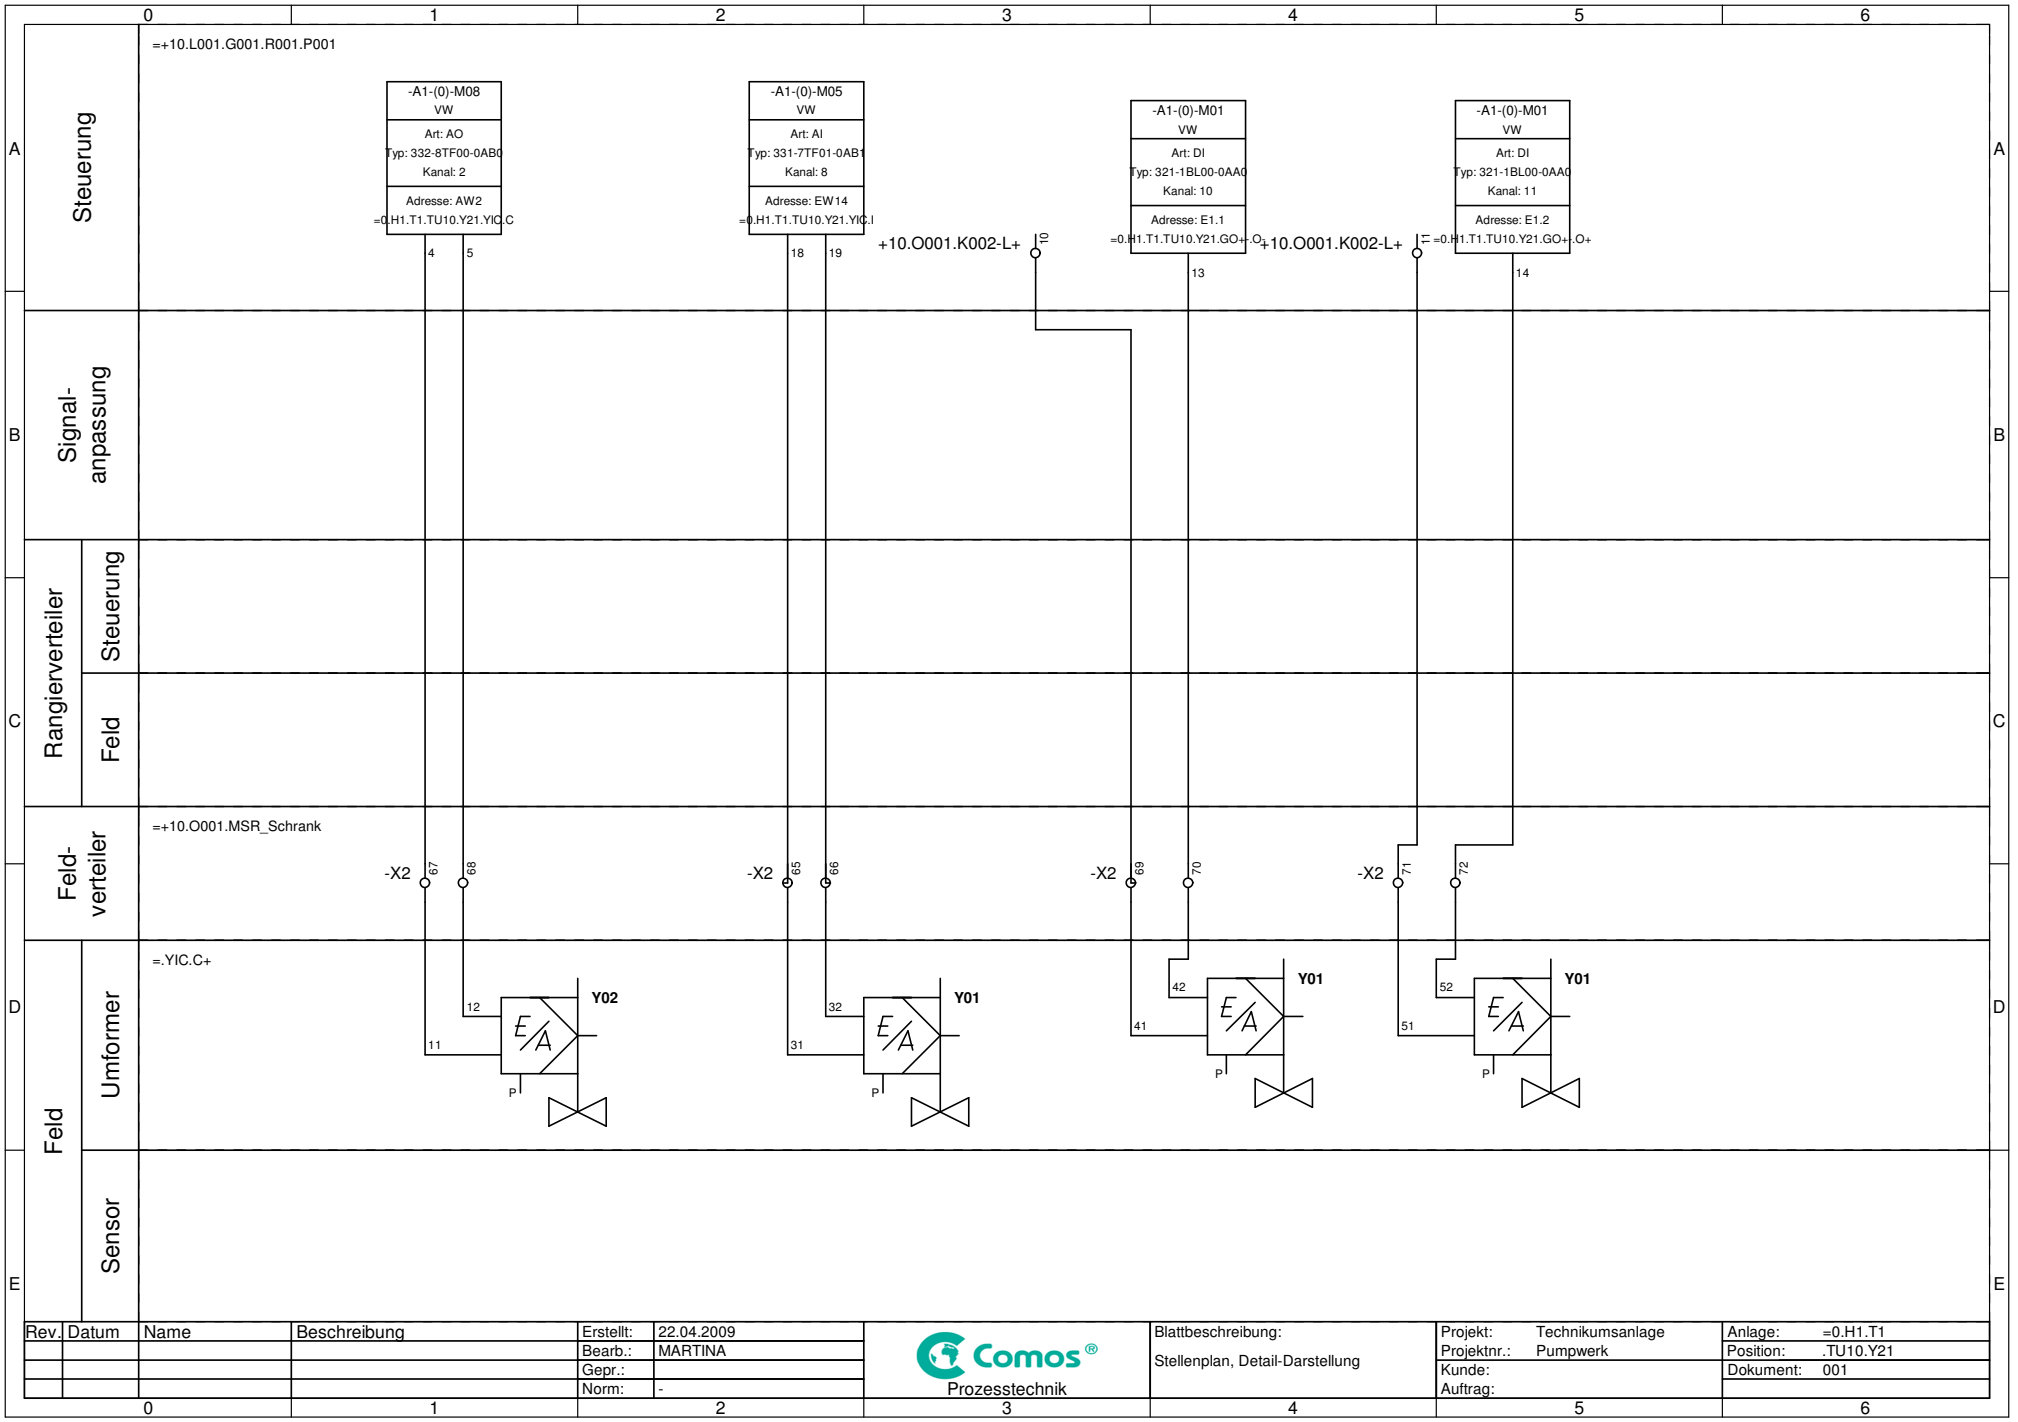


Rev.	Datum	Name	Beschreibung		
				Erstellt:	22.04.2009
				Bearb.:	MARTINA
				Gepr.:	
				Norm:	-

Comos® Prozesstechnik

Blattbeschreibung: Stellenplan, Detail-Darstellung

Projekt:	Technikumsanlage
Projektnr.:	Pumpwerk
Kunde:	
Auftrag:	

Anlage:	=0.H1.T1
Position:	.TU10.Y21
Dokument:	001